


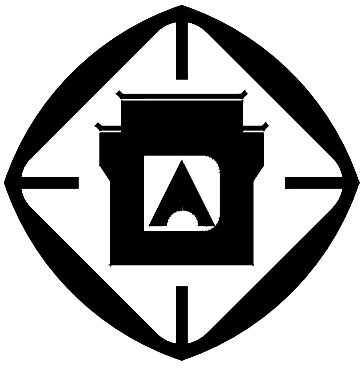

安徽省建筑设计研究总院股份有限公司

合作设计单位

注册师印章

会签专业	会签(正楷)	
建 筑	刘 静	
结 构	沈 文 杰	
给 排 水	钱 坤	
暖 通	谢 亦 伟	
电 气		

出图专用章


审 定	谢正荣	
审 核	谢正荣	
工程主持人	王红兵 刘 静	
方案设计人		
专业负责人	谢正荣	
校 对	汪 军	
设 计	伍 葵	
制 图	伍 葵	

工程编号	2020113
建设单位	安徽医科大学第一附属医院东区 (肥东县人民医院)
工程名称	安徽医科大学第一附属医院东区 (肥东县人民医院) 公共卫生综合楼
子项名称	

标 题:

四层电气消防平面图

日 期	2020 年 11 月 11 日		
比 例	见 图		
设计阶段	施工图		
专业及类别	电施	图号	80
版本	A版		83

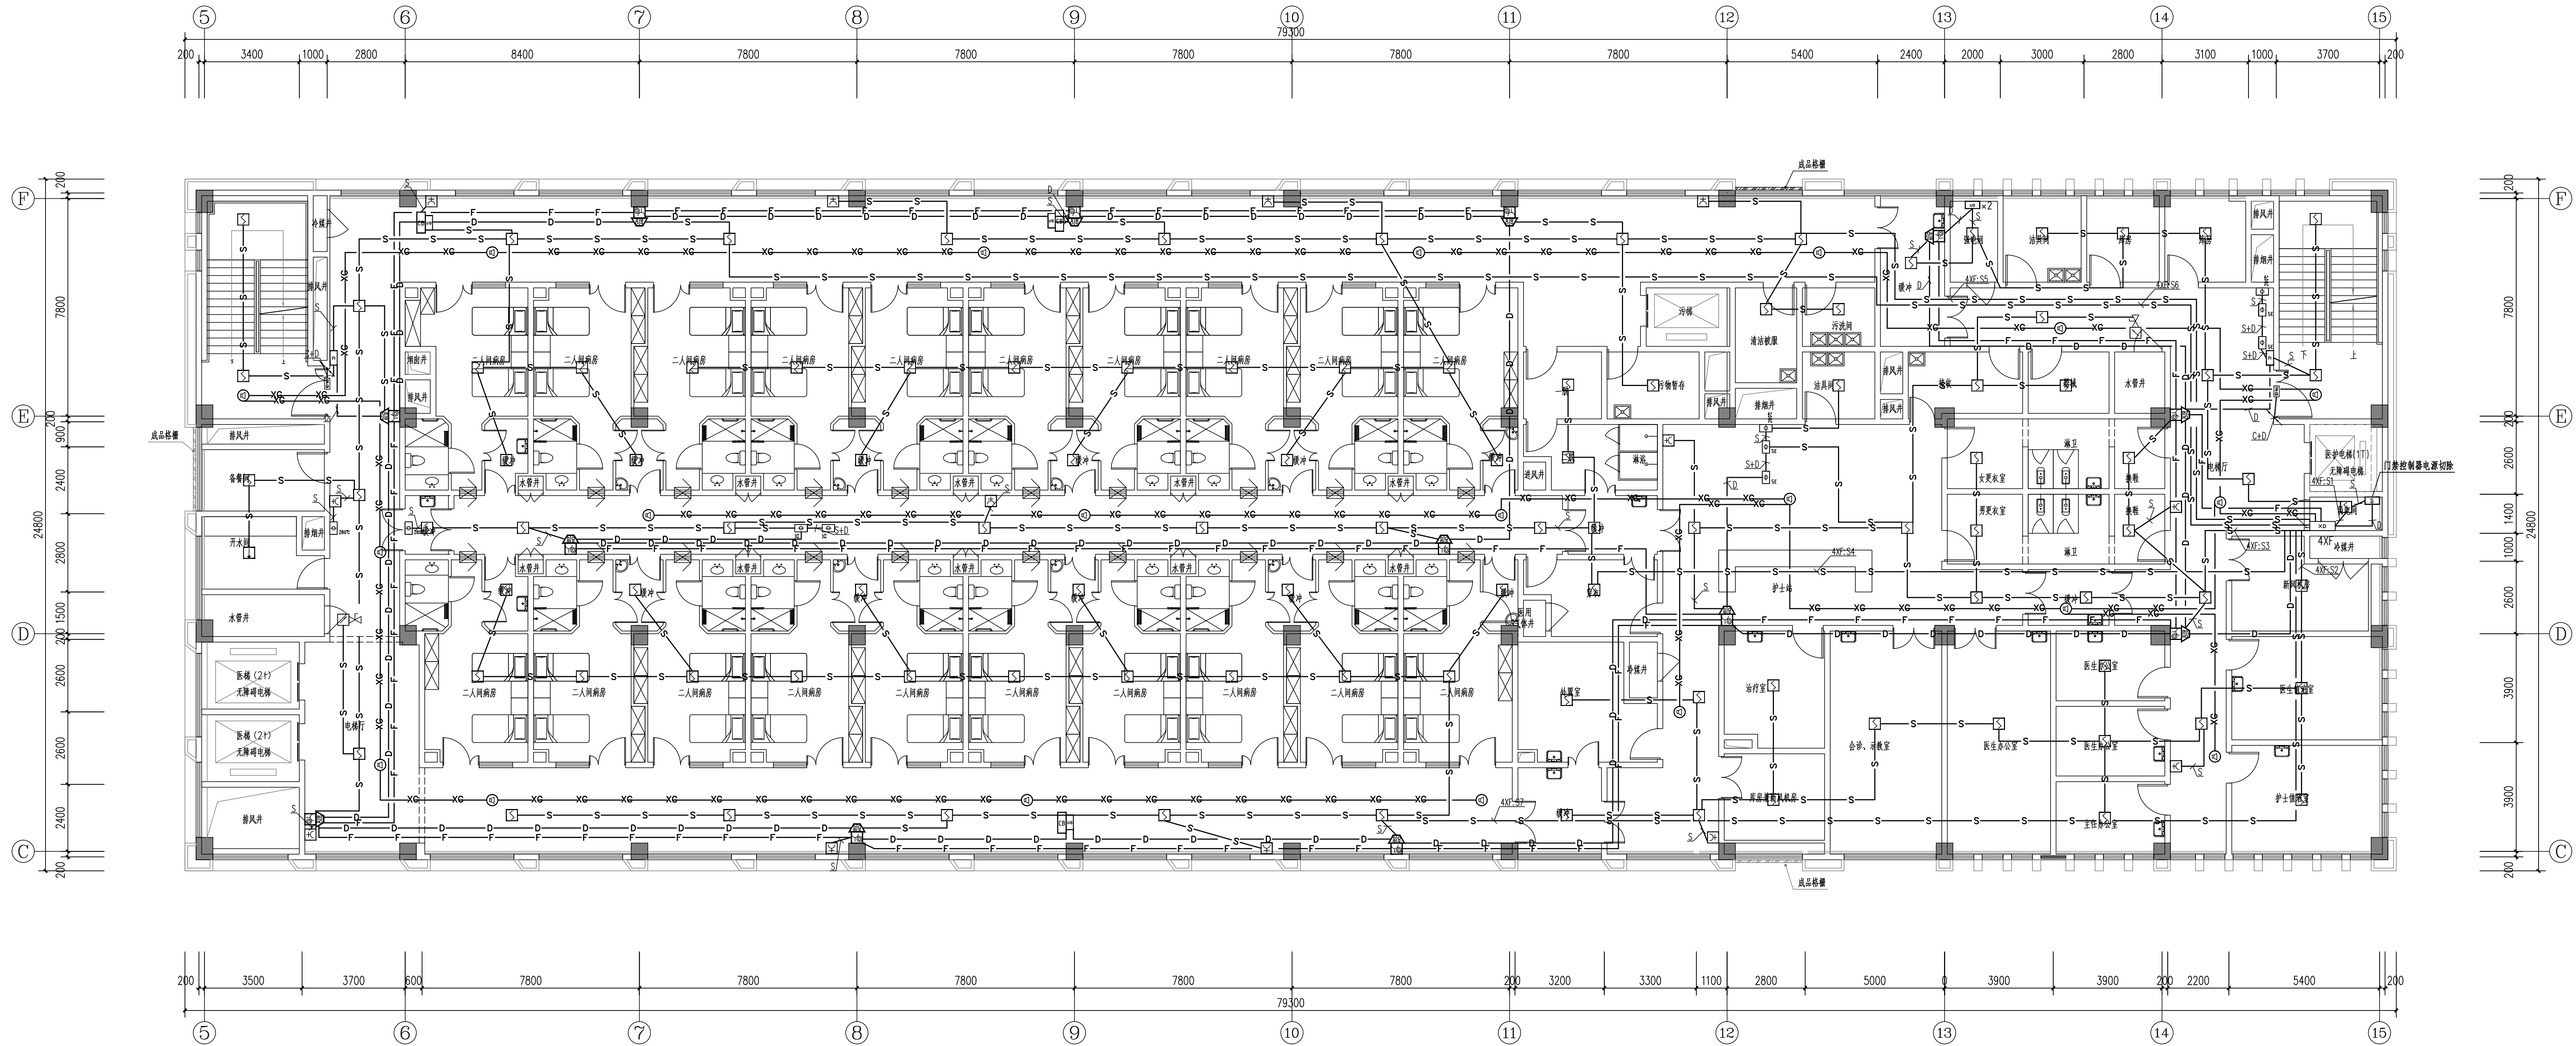

四层电气消防平面图 1:100

注1: 平战结合+区的重症监护病房、负压病房、检验室、生物安全实验室等区域穿墙和楼板的线缆加套管或采用专用电缆穿墙装置,管内采用无腐蚀性、不燃、弹性材料封堵。
注2: 防辐射隔墙及楼板上照明插座管线明敷,开关插座后期明装,穿墙和楼板的管线两侧设钢板管内用不燃防辐射材料密封,管路过墙形成弯折。
注3: 本平面图S+D表示信号总线+DC24V电源总线,分开穿管,2SC20